


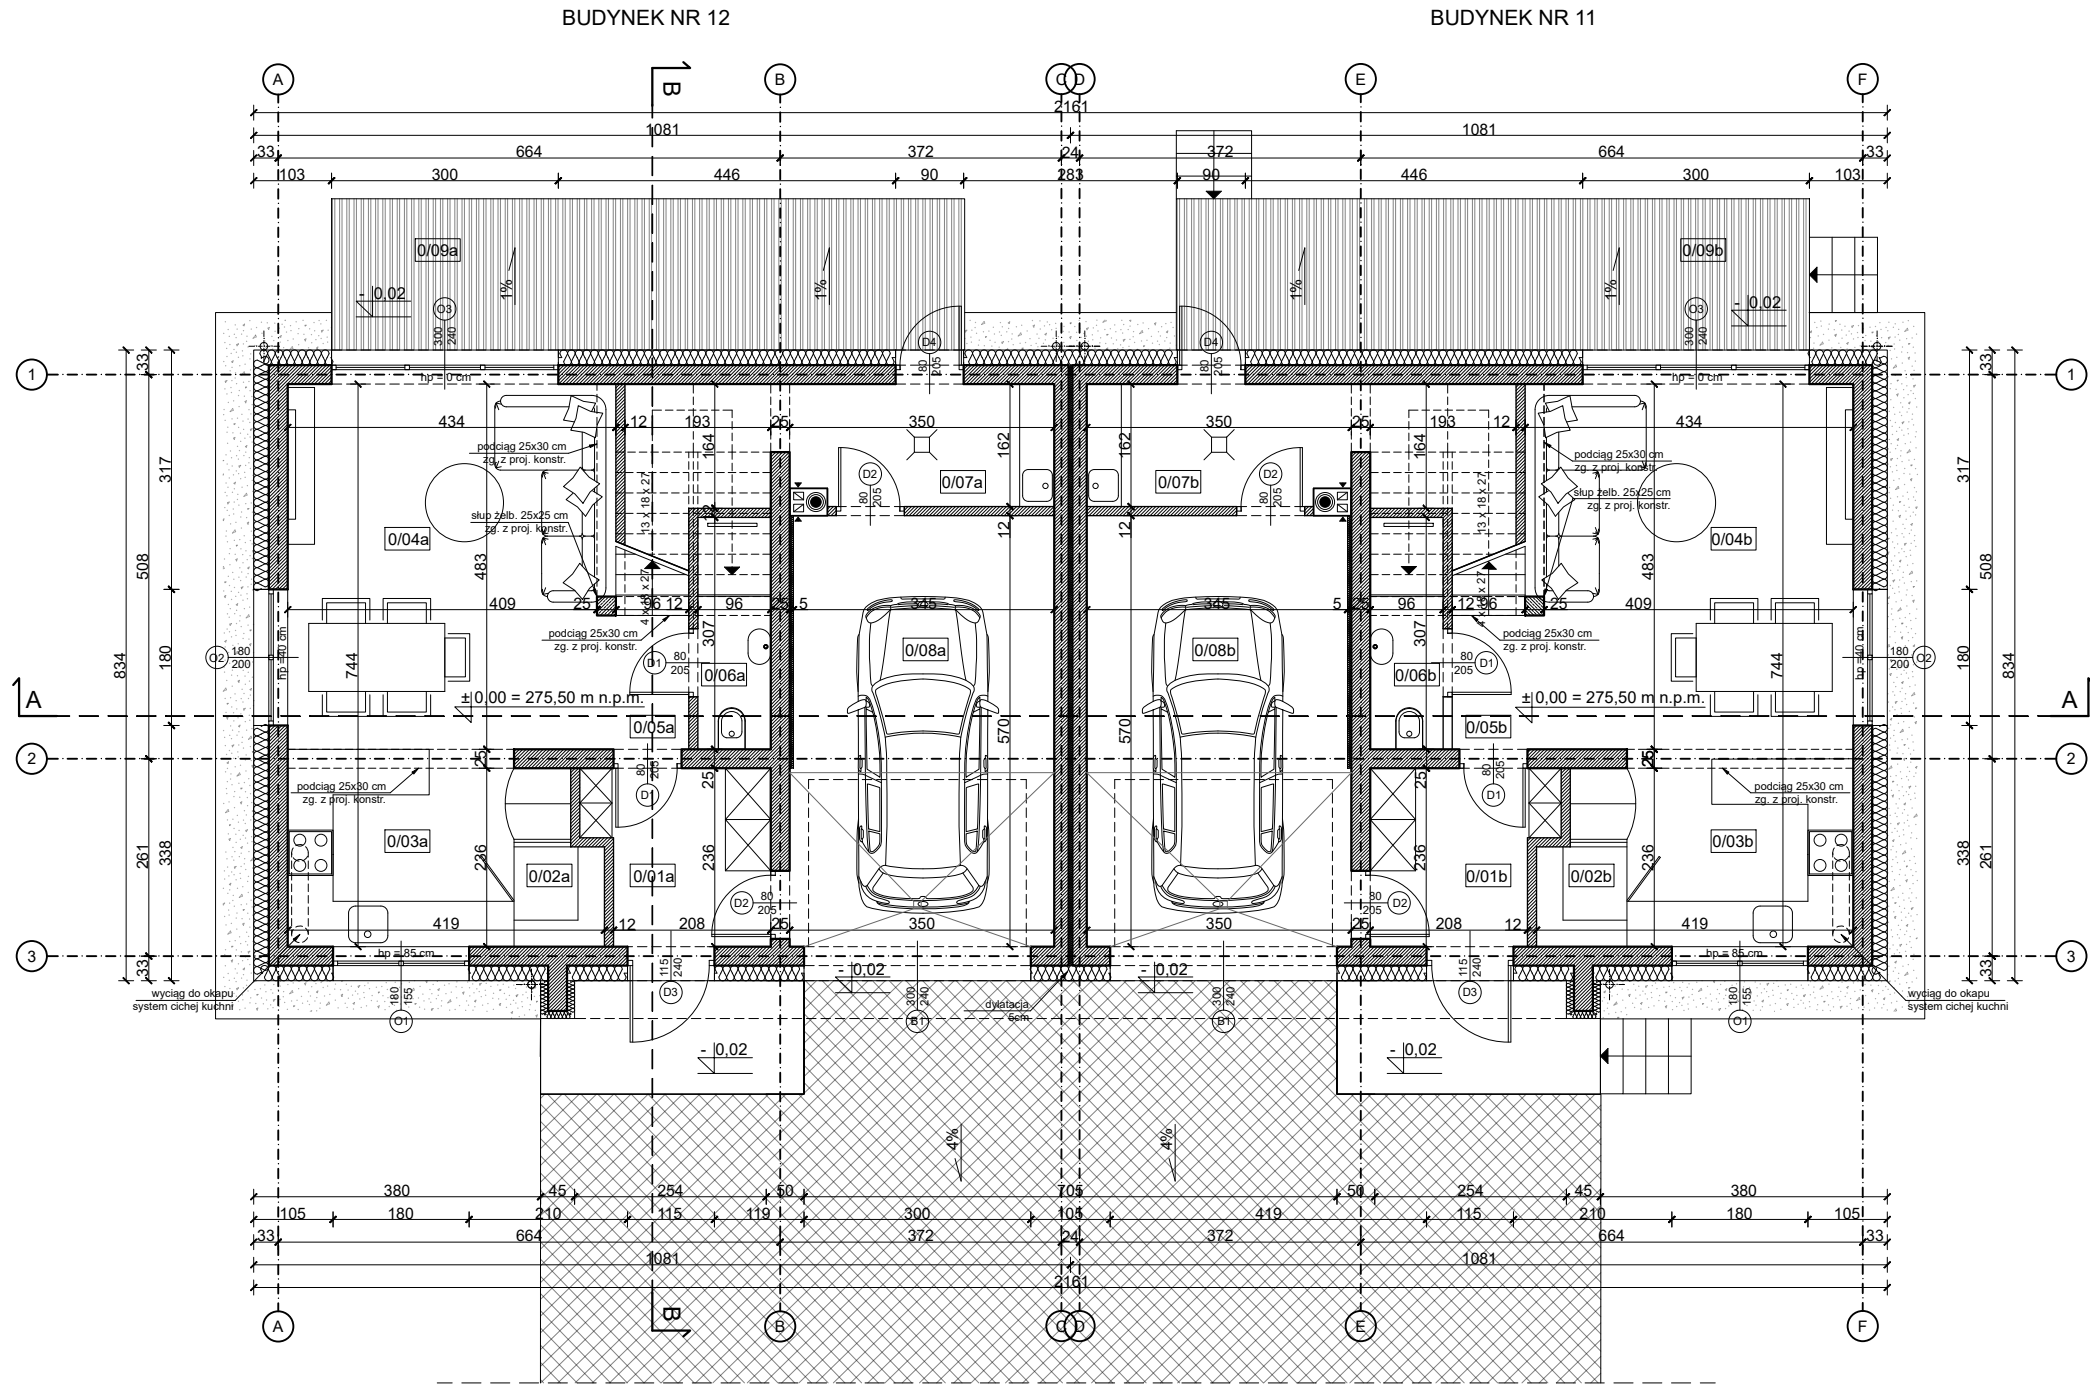

PARTER - ZESTAWIENIE POMIESZCZEŃ - BUDYNEK NR 11			
	pomieszczenie	posadzka	pow. użyt. [m²]
0/01b	WIATROŁAP	PLYTKI GRESOWE	5,17
0/02b	SPIŻARNIA	PLYTKI GRESOWE	1,50
0/03b	KUCHNIA	PLYTKI GRESOWE	8,49
0/04b	SALON Z JADALNIĄ	PANELE PODŁOGOWE	20,70
0/05b	KOMUNIKACJA	PLYTKI GRESOWE	4,68
0/06b	ŁAZIENKA	PLYTKI GRESOWE	2,84
0/07b	POM. GOSP.	PLYTKI GRESOWE	6,42
0/08b	GARAŻ	PLYTKI GRESOWE	19,67
SUMA			69,47
0/09b	TARAS	PLYTY TARASOWE	16,75

PARTER - ZESTAWIENIE POMIESZCZEŃ - BUDYNEK NR 12			
	pomieszczenie	posadzka	pow. użyt. [m²]
0/01a	WIATROŁAP	PLYTKI GRESOWE	5,17
0/02a	SPIŻARNIA	PLYTKI GRESOWE	1,50
0/03a	KUCHNIA	PLYTKI GRESOWE	8,49
0/04a	SALON Z JADALNIĄ	PANELE PODŁOGOWE	20,70
0/05a	KOMUNIKACJA	PLYTKI GRESOWE	4,68
0/06a	ŁAZIENKA	PLYTKI GRESOWE	2,84
0/07a	POM. GOSP.	PLYTKI GRESOWE	6,42
0/08a	GARAŻ	PLYTKI GRESOWE	19,67
SUMA			69,47
0/09a	TARAS	PLYTY TARASOWE	16,75

WYMIARY STOLARKI

OKNA - podano wymiary w świetle ościeży (otwór w ścianie w stanie surowym)

DRZWI - podano wymiary w świetle ościeżnicy (światło futryny drzwiowej)
Grubość skrzydła drzwi po otwarciu nie może pomniejszyć wymiaru szerokości otworu w świetle ościeżnicy

UWAGI:

- Wszystkie wymiary sprawdzić na budowie.
- Rysunek stanowi część pełnobrańowego projektu budowlanego, należy go rozpatrzyć łącznie z opisem technicznym i projektami branżowymi.
- Wszystkie elementy stalowe zabezpieczyć antykorozyjnie i ppoż zgodnie ze sztuką budowlaną oraz obowiązującymi normami.
- Głębokość posadowienia zweryfikować na budowie. W razie jakichkolwiek niezgodności należy skonsultować się z projektantem.
- Wszystkie zaprojektowane elementy wykonać zgodnie ze sztuką budowlaną i wytycznymi przyjętych systemów.
- Izolacje wykonać zgodnie ze sztuką budowlaną zapewniając ich ciągłość.
- W przypadku wystąpienia gruntów spoistych w podłożu zaleca się wykonanie drenażu opaskowego.
- Odprowadzanie wody opadowej z połączy dachu poza obrys fundamentów.
- Możliwość zamontowania rolet podtynkowych.

PRACOWNIA PROJEKTOWA ARCHIKABA
UL. LEDNICKA 31 32-020 WIELICZKA T: 512 64 95 54

Temat:

"BUDOWA 2 BUDYNKÓW MIESZKALNYCH JEDNORODZINNYCH nr 11 i 12, JEDNOLOKALOWYCH W ZABUDOWIE BLIŹNIACZEJ WRAZ Z ZEWNĘTRZNYMI ODCINKAMI WEWNĘTRZNYCH INSTALACJI: EN. ELEKTRYCZNEJ, GAZU, KANALIZACJI SANITARNEJ WRAZ Z 2 SZCZELNYMI ZBIORNIKAMI NA NIECZYSTOŚCI CIEKŁE, KANALIZACJI DESZCZOWEJ WRAZ Z 4 SZCZELNYMI ZBIORNIKAMI NA WODY OPADOWE ORAZ BUDOWĄ UTWARDZONEGO DOJŚCIA I DOJAZDU NA DZ. NR EWID. 600/59, OBRĘB 0010 ZAGÓRZE, JEDNOSTKA EWIDENCYJNA 121904_5 NIEPOŁOMICE-G, MIEJSCOWOŚĆ ZAGÓRZE"

Lokalizacja: DZIAŁKA NR EWID. 600/59, OBRĘB NR 0010 ZAGÓRZE, JEDN. EWID. 121904_5 NIEPOŁOMICE-G, W MIEJSCOWOŚCI ZAGÓRZE	Faza: PAB
Projektant: mgr inż. arch. Katarzyna Machaj nr upr. MPOIA/025/2018	Podpis: Branża: ARCHITEKTURA
Opracował: inż. arch. Kinga Malendowicz	Podpis: Data: PAŹDZIERNIK 2024
Opracował: mgr inż. arch. Alicja Schacherer	Podpis: Skala: 1:100
Tytuł rys.: RZUT PARTERU	Nr rys.: A 01