


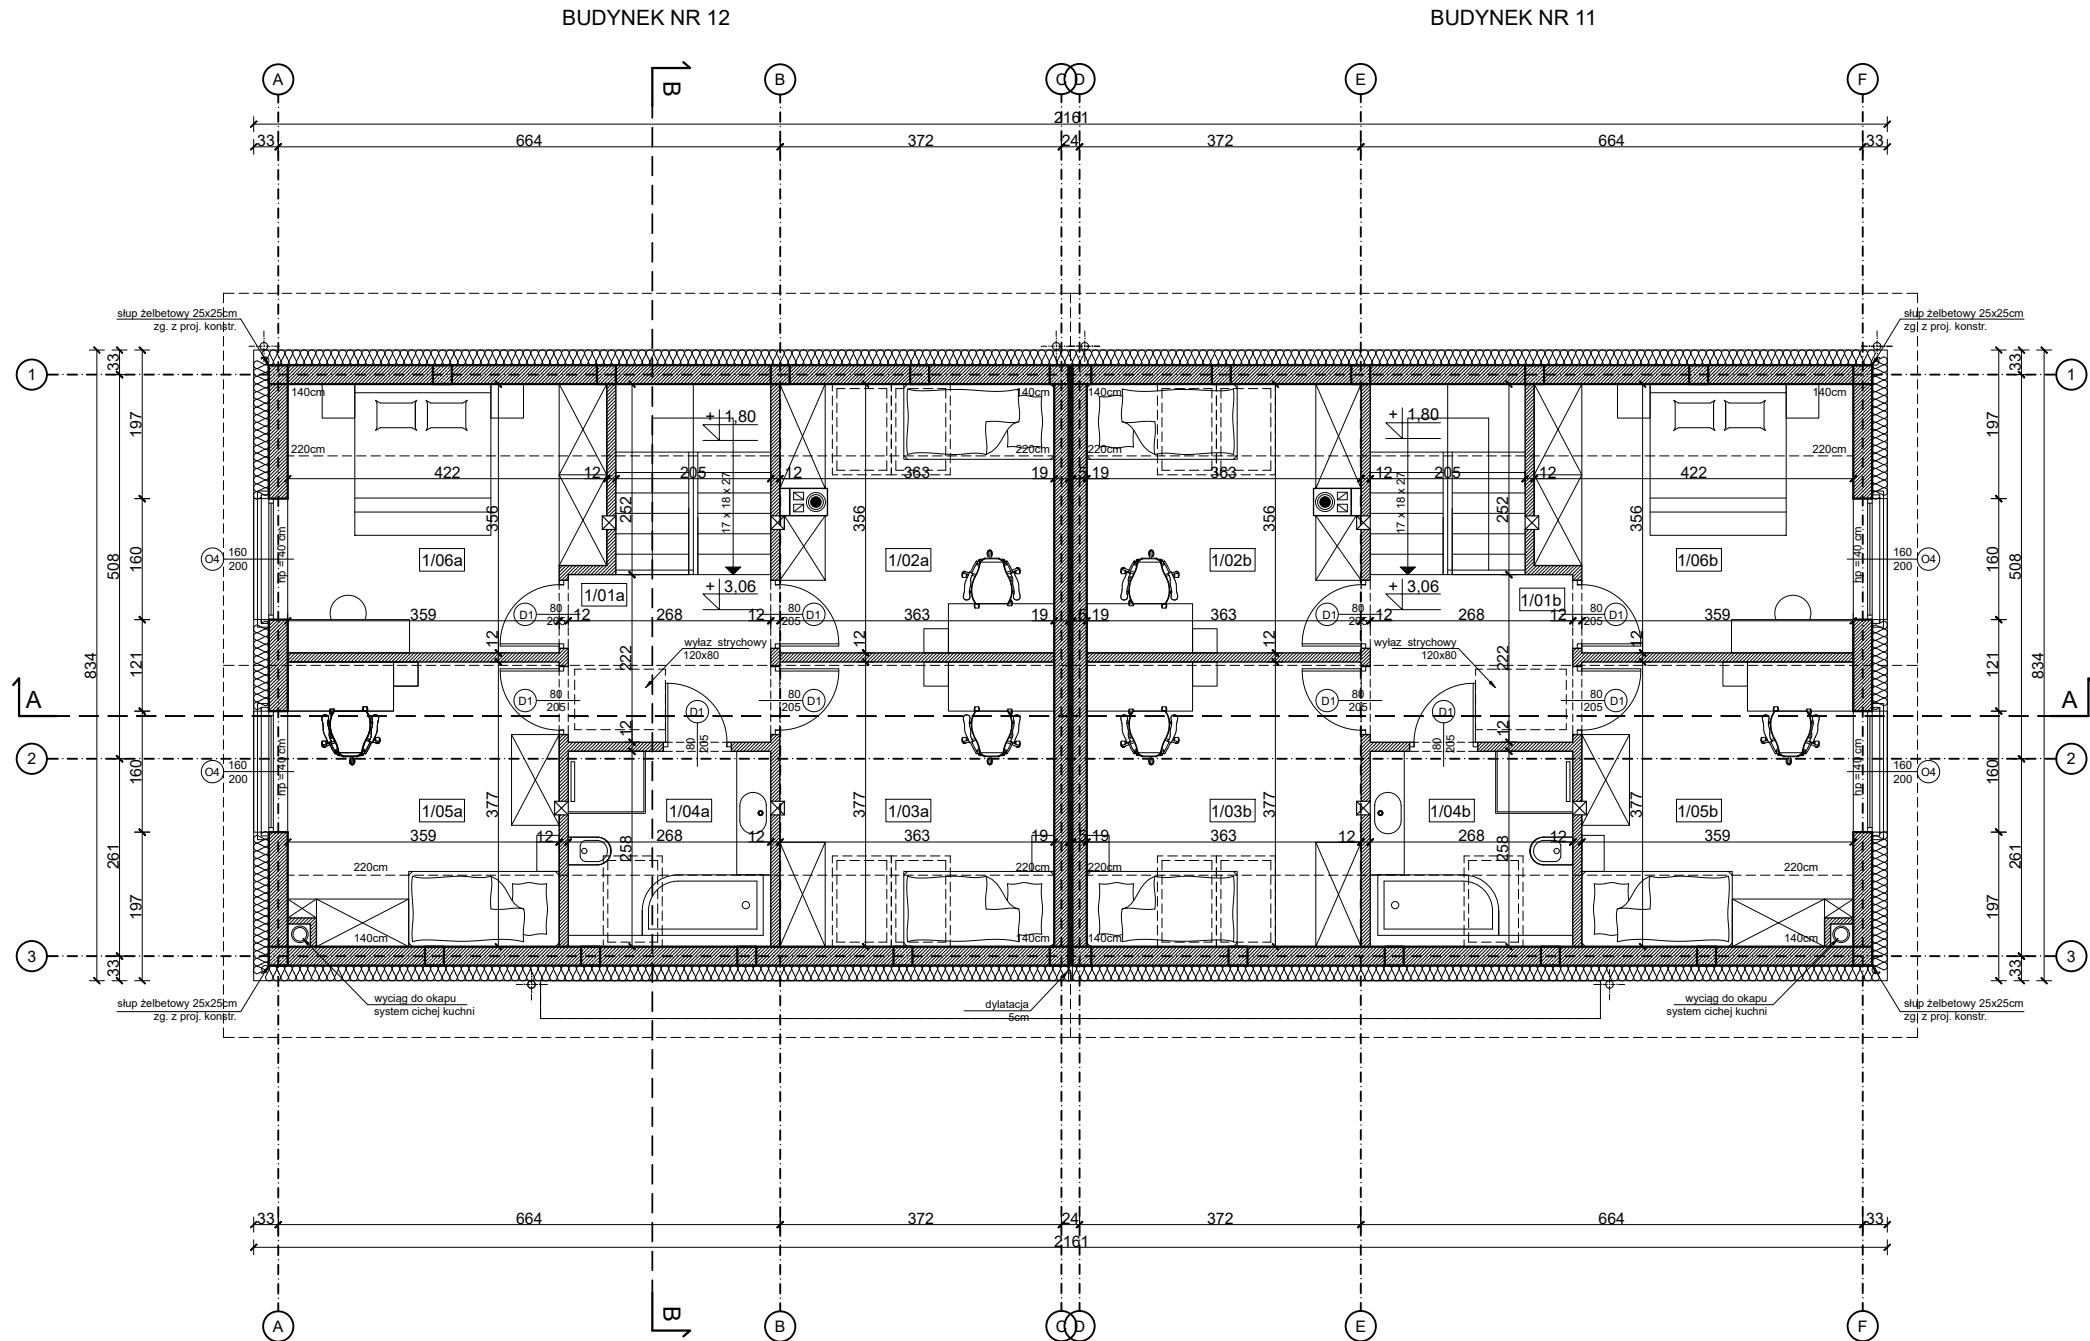

PODDASZE - ZESTAWIENIE POMIESZCZEŃ - BUDYNEK NR 11			
	pomieszczenie	posadzka	pow.użyt. [m²]
1/01b	KOMUNIKACJA	PANELE PODŁOGOWE	8,21
1/02b	POKÓJ	PANELE PODŁOGOWE	11,20
1/03b	POKÓJ	PANELE PODŁOGOWE	12,22
1/04b	ŁAZIENKA	PŁYTKI GRESOWE	5,75
1/05b	POKÓJ	PANELE PODŁOGOWE	11,60
1/06b	SYPIALNIA	PANELE PODŁOGOWE	12,04
SUMA			61,02
SUMA POWIERZCHNI BUDYNKU NR 11			130,49

PODDASZE - ZESTAWIENIE POMIESZCZEŃ - BUDYNEK NR 12			
	pomieszczenie	posadzka	pow.użyt. [m²]
1/01a	KOMUNIKACJA	PANELE PODŁOGOWE	8,21
1/02a	POKÓJ	PANELE PODŁOGOWE	11,20
1/03a	POKÓJ	PANELE PODŁOGOWE	12,22
1/04a	ŁAZIENKA	PŁYTKI GRESOWE	5,75
1/05a	POKÓJ	PANELE PODŁOGOWE	11,60
1/06a	SYPIALNIA	PANELE PODŁOGOWE	12,04
SUMA			61,02
SUMA POWIERZCHNI BUDYNKU NR 12			130,49

WYMIARY STOLARKI

OKNA - podano wymiary w świetle ościeży (otwór w ścianie w stanie surowym)

DRZWI - podano wymiary w świetle ościeżnicy (światło futryny drzwiowej)
Grubość skrzydła drzwi po otwarciu nie może pomniejszyć wymiaru szerokości otworu w świetle ościeżnicy

UWAGI:

1. Wszystkie wymiary sprawdzić na budowie.
2. Rysunek stanowi część pełnobrańowego projektu budowlanego, należy go rozpatrzyć łącznie z opisem technicznym i projektami branżowymi.
3. Wszystkie elementy stalowe zabezpieczyć antykorozyjnie i ppoż zgodnie ze sztuką budowlaną oraz obowiązującymi normami.
4. Głębokość posadowienia zweryfikować na budowie. W razie jakichkolwiek niezgodności należy skonsultować się z projektantem.
5. Wszystkie zaprojektowane elementy wykonać zgodnie ze sztuką budowlaną i wytycznymi przyjętych systemów.
6. Izolacje wykonać zgodnie ze sztuką budowlaną zapewniając ich ciągłość.
7. W przypadku wystąpienia gruntów spoistych w podłożu zaleca się wykonanie drenażu opaskowego.
8. Odprowadzanie wody opadowej z połąci dachu poza obrys fundamentów.
9. Możliwość zamontowania rolet podtynkowych.

PRACOWNIA PROJEKTOWA ARCHIKABA
UL. LEDNICKA 31 32-020 WIELICZKA T: 512 64 95 54

Temat:

"BUDOWA 2 BUDYNKÓW MIESZKALNYCH JEDNORODZINNYCH nr 11 i 12, JEDNOLOKALOWYCH W ZABUDOWIE BLIŹNIACZEJ WRAZ Z ZEWNĘTRZNYMI ODCINKAMI WEWNĘTRZNYCH INSTALACJI: EN. ELEKTRYCZNEJ, GAZU, KANALIZACJI SANITARNEJ WRAZ Z 2 SZCZELNYMI ZBIORNIKAMI NA NIECZYSTOŚCI CIEKŁE, KANALIZACJI DESZCZOWEJ WRAZ Z 4 SZCZELNYMI ZBIORNIKAMI NA WODY OPADOWE ORAZ BUDOWĄ UTWARDZONEGO DOJŚCIA I DOJAZDU NA DZ. NR EWID. 600/59, OBRĘB 0010 ZAGÓRZE, JEDNOSTKA EWIDENCYJNA 121904_5 NIEPOŁOMICE-G, MIEJSCOWOŚĆ ZAGÓRZE"

Lokalizacja: DZIAŁKA NR EWID. 600/59, OBRĘB NR 0010 ZAGÓRZE, JEDN. EWID. 121904_5 NIEPOŁOMICE-G, W MIEJSCOWOŚCI ZAGÓRZE	Faza: PAB
Projektant: mgr inż. arch. Katarzyna Machaj nr upr. MPOIA/025/2018	Podpis: Branża: ARCHITEKTURA
Opracował: inż. arch. Kinga Malendowicz	Podpis: Data: PAŹDZIERNIK 2024
Opracował: mgr inż. arch. Alicja Schacherer	Podpis: Skala: 1:100
Tytuł rys.: RZUT PODDASZA	Nr rys.: A 02