


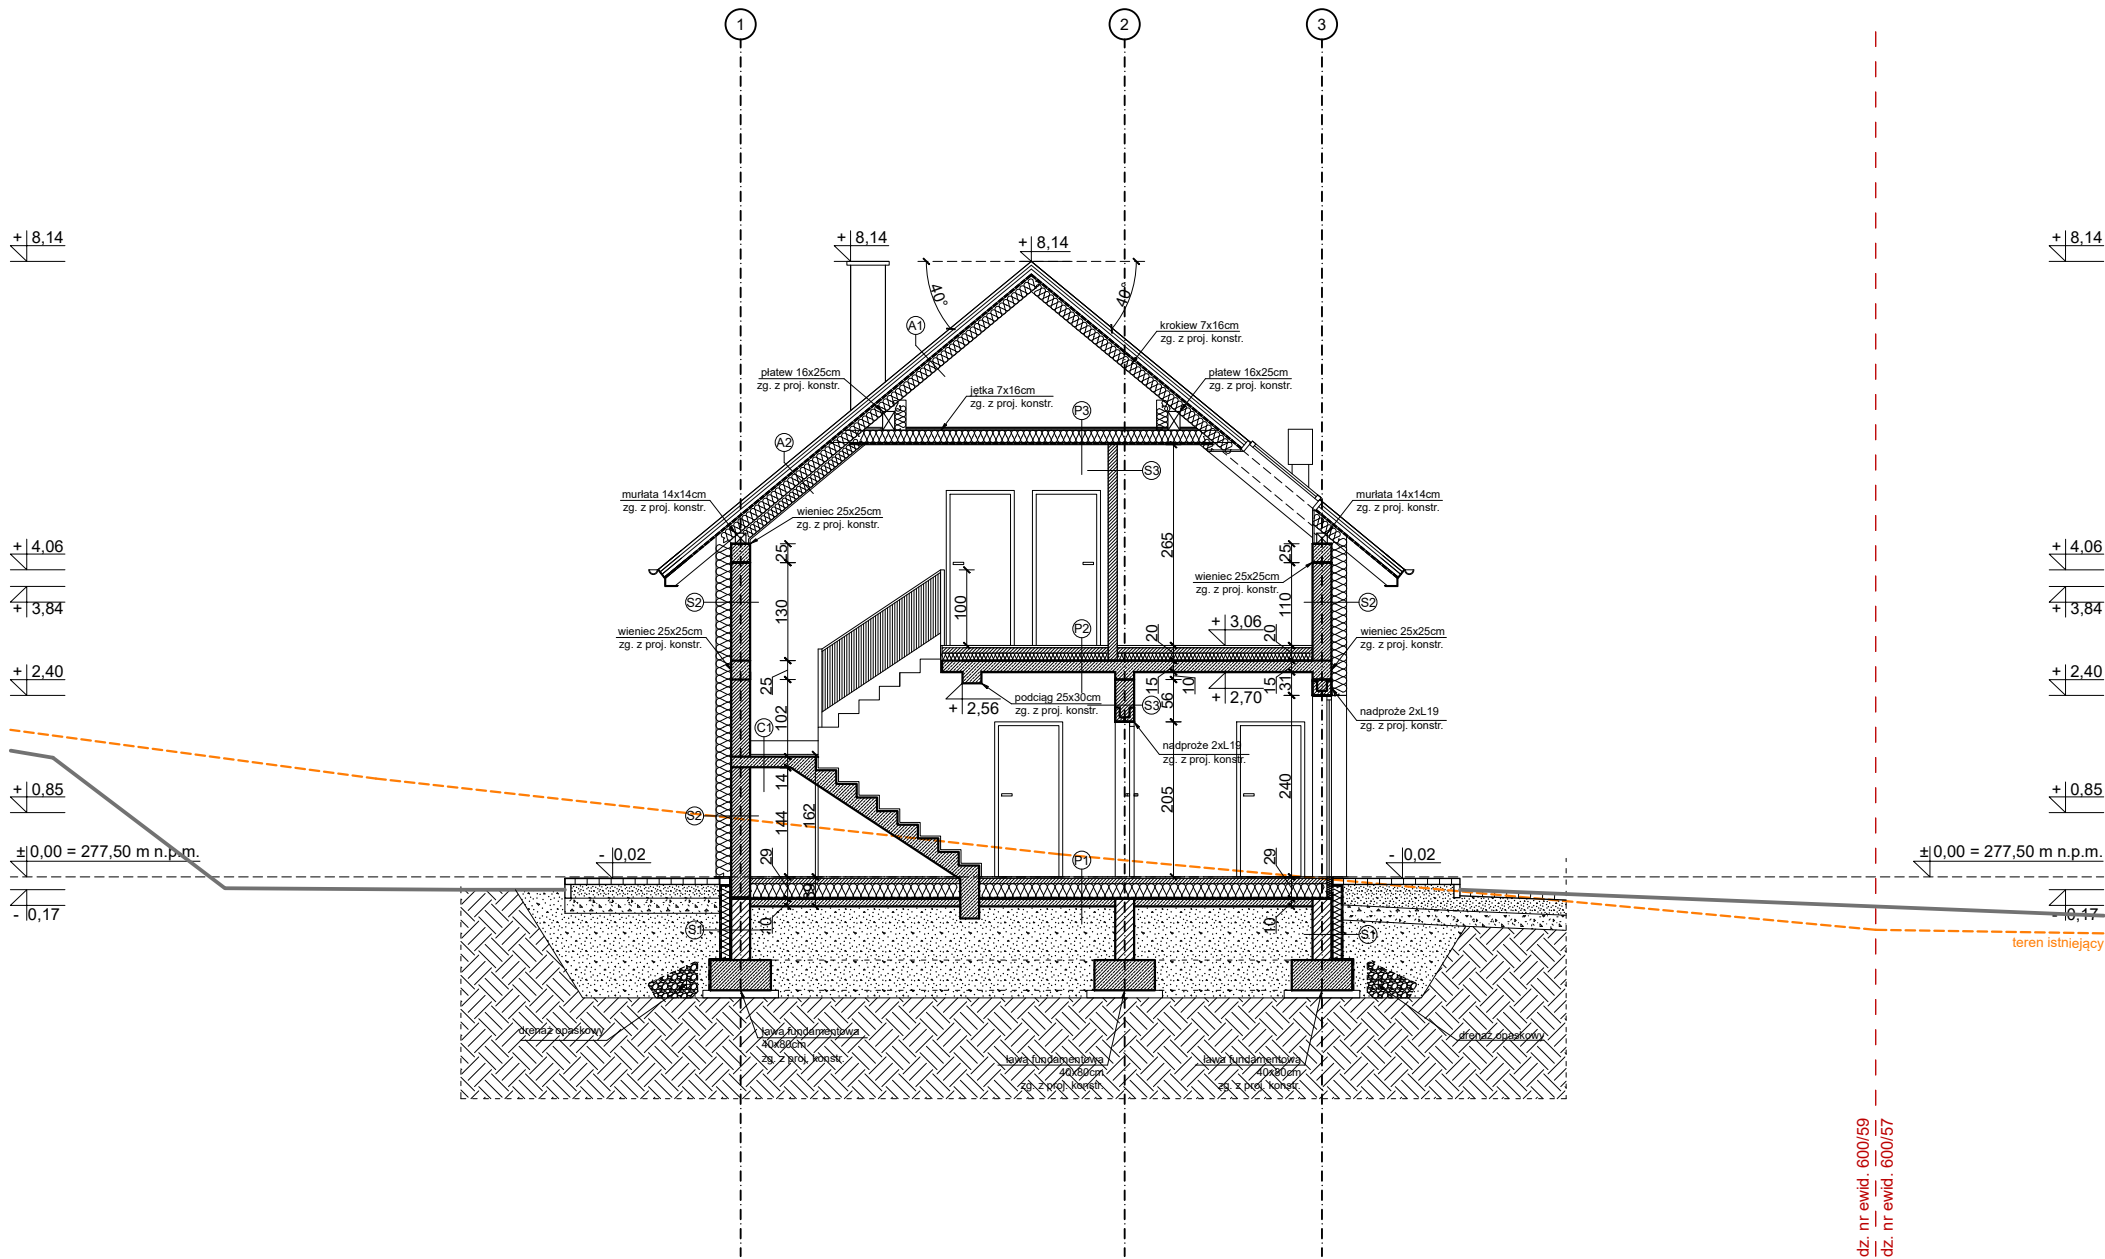

WYMIARY STOLARKI
OKNA - podano wymiary w świetle ościeży (otwór w ścianie w stanie surowym)
DRZWI - podano wymiary w świetle ościeżnicy (światło futryny drzwiowej) Grubość skrzydła drzwi po otwarciu nie może pomniejszyć wymiaru szerokości otworu w świetle ościeżnicy

- UWAGI:**
1. Wszystkie wymiary sprawdzić na budowie.
 2. Rysunek stanowi część pełnobrańzowego projektu budowlanego, należy go rozpatrzyć łącznie z opisem technicznym i projektami branżowymi.
 3. Wszystkie elementy stalowe zabezpieczyć antykorozyjnie i ppoż zgodnie ze sztuką budowlaną oraz obowiązującymi normami.
 4. Głębokość posadowienia zweryfikować na budowie. W razie jakichkolwiek niezgodności należy skonsultować się z projektantem.
 5. Wszystkie zaprojektowane elementy wykonać zgodnie ze sztuką budowlaną i wytycznymi przyjętych systemów.
 6. Izolacje wykonać zgodnie ze sztuką budowlaną zapewniając ich ciągłość.
 7. W przypadku wystąpienia gruntów spoistych w podłożu zaleca się wykonanie drenażu opaskowego.
 8. Odprowadzanie wody opadowej z połaci dachu poza obrys fundamentów.
 9. Możliwość zamontowania rolet podtynkowych.

A1 DACH zg. z proj. konstr.	P1 PODŁOGA NA GRUNCIE zg. z proj. konstr.	C1 SCHODY zg. z proj. konstr.	S3 ŚCIANA WEWNĘTRZNA zg. z proj. konstr.
- DACHÓWKA CERAMICZNA - FOLIA IZOLACYJNA - 3 x 4 ŁATY - 5 x 4 KONTRŁATY - FOLIA PAROPRZEPUSZCZALNA - 7 x 16 KROKIEW - FOLIA POLIETYLENOWA	- 2cm PANELE PODŁ./PŁYTKI CERAMICZNE - 7cm WYLEWKA CEMENTOWA ZBROJONA - 20cm STYROPIAN XPS - 2 x PAPA TERMOZGRZEWALNA PODKŁADOWA - 10cm BETON C12/15 - PODSYPKA ŻWIROWO-PIASKOWA min. 30cm	- DREWNIANA STOPNICA - 14 CM PŁYTA ŻELBETOWA - TYNK CEMENTOWO-WAPIENNY	- TYNK CEMENTOWO-WAPIENNY - 12 / 25 CM PUSTAK CERAMICZNY - TYNK CEMENTOWO- WAPIENNY
A2 DACH zg. z proj. konstr.	P2 STROP NAD PARTEREM zg. z proj. konstr.	S1 ŚCIANA FUNDAMENTOWA zg. z proj. konstr.	S4 ŚCIANA WEWNĘTRZNA MIĘDZY BUDYNKAMI zg. z proj. konstr.
- DACHÓWKA CERAMICZNA - FOLIA IZOLACYJNA - 3 x 4 ŁATY - 5 x 4 KONTRŁATY - FOLIA PAROPRZEPUSZCZALNA - 7x16 KROKIEW/30 cm WEŁNA MINERALNA - FOLIA POLIETYLENOWA - PŁYTA G-K NA KONSTRUKCJI STALOWEJ	- 2 cm PANELE PODŁ./PŁYTKI CERAMICZNE - 7cm WYLEWKA CEMENTOWA ZBROJONA - 10cm STYROPIAN EPS - FOLIA POLIETYLENOWA - 15 cm PŁYTA ŻELBETOWA - TYNK CEMENTOWO-WAPIENNY	- FOLIA KUBEŁKOWA - 15cm STYROPIAN XPS - IZOLACJA PRZECIWWILGOCIOWA - 25 cm PUSTAK BETONOWY - WARSTWA GRUNTU ZASYPOWEGO, ZAGĘSZCZONEGO MECHANICZNIE	- TYNK CEMENTOWO-WAPIENNY - 19 CM PUSTAK CERAMICZNY - 5 CM DYLATACJA STYROPIAN XPS - 19 CM PUSTAK CERAMICZNY - TYNK CEMENTOWO-WAPIENNY
	P3 STROP NAD PODDASZEM	S2 ŚCIANA ZEWNĘTRZNA zg. z proj. konstr.	
	- 2 x PŁYTA OSB - RUSZT DREWNIANY/ 14 CM WEŁNA MINERALNA - 7x16cm JĘTKI DREWNIANE/ WEŁNA MINERALNA - FOLIA POLIETYLENOWA - PŁYTY G-K NA KONSTRUKCJI STALOWEJ	- TYNK SILIKATOWO-SILIKONOWY - 20 CM STYROPIAN EPS 100 - 25 CM PUSTAK CERAMICZNY - TYNK CEMENTOWO- WAPIENNY	

PRACOWNIA PROJEKTOWA ARCHIKABA UL. LEDNICKA 31 32-020 WIELICZKA T: 512 64 95 54			
Temat: "BUDOWA 2 BUDYNKÓW MIESZKALNYCH JEDNORODZINNYCH nr 11 i 12, JEDNOLOKALOWYCH W ZABUDOWIE BLIŹNIACZEJ WRAZ Z ZEWNĘTRZNYMI ODCINKAMI WEWNĘTRZNYCH INSTALACJI: EN. ELEKTRYCZNEJ, GAZU, KANALIZACJI SANITARNEJ WRAZ Z 2 SZCZELNYMI ZBIORNIKAMI NA NIECZYSTOŚCI CIEKŁE, KANALIZACJI DESZCZOWEJ WRAZ Z 4 SZCZELNYMI ZBIORNIKAMI NA WODY OPADOWE ORAZ BUDOWĄ UTWARDZONEGO DOJŚCIA I DOJAZDU NA DZ. NR EWID. 600/59, OBRĘB 0010 ZAGÓRZE, JEDNOSTKA EWIDENCYJNA 121904_5 NIEPOŁOMICZE-G, MIEJSCOWOŚĆ ZAGÓRZE"			
Lokalizacja: DZIAŁKA NR EWID. 600/59, OBRĘB NR 0010 ZAGÓRZE, JEDN. EWID. 121904_5 NIEPOŁOMICZE-G, W MIEJSCOWOŚCI ZAGÓRZE	Faza: PAB		
Projektant: mgr inż. arch. Katarzyna Machaj nr upr. MPOIA/025/2018	Podpis:	Branża: ARCHITEKTURA	
Opracował: inż. arch. Kinga Malendowicz	Podpis:	Data: PAŹDZIERNIK 2024	
Opracował: mgr inż. arch. Alicja Schacherer	Podpis:	Skala: 1:100	
Tytuł rys.: PRZEKRÓJ B-B		Nr rys.: A 05	